



TOTAL GROSS SQUARE FOOTAGE	
1ST FLOOR:	1,009 SF
2ND FLOOR:	1,435 SF
TOTAL FINISHED:	2,440 SF
GARAGE:	528 SF
UNFINISHED BASEMENT:	908 SF

1ST FLOOR AREA PLAN

2ND FLOOR AREA PLAN

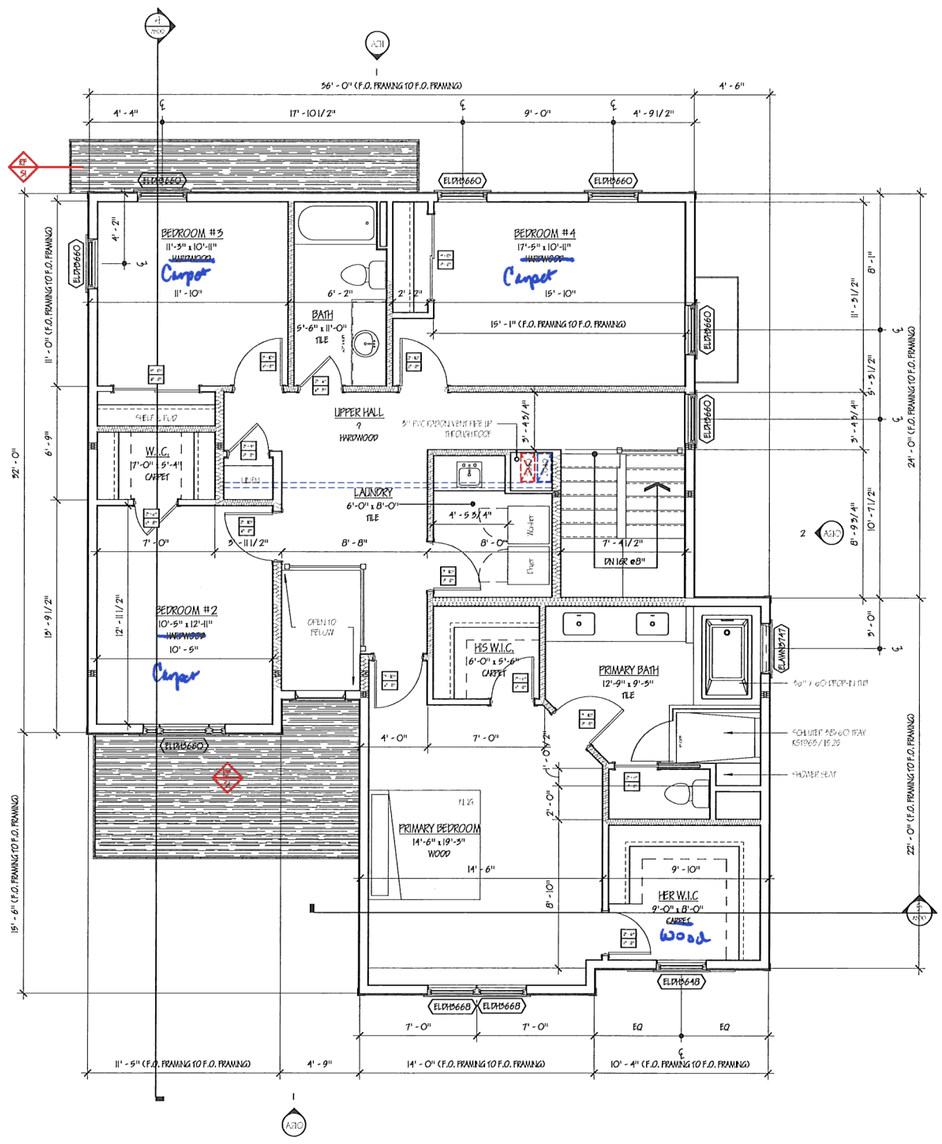

2 CONSTRUCTION PLAN - 2ND FLOOR
SCALE: 1/4" = 1'-0"

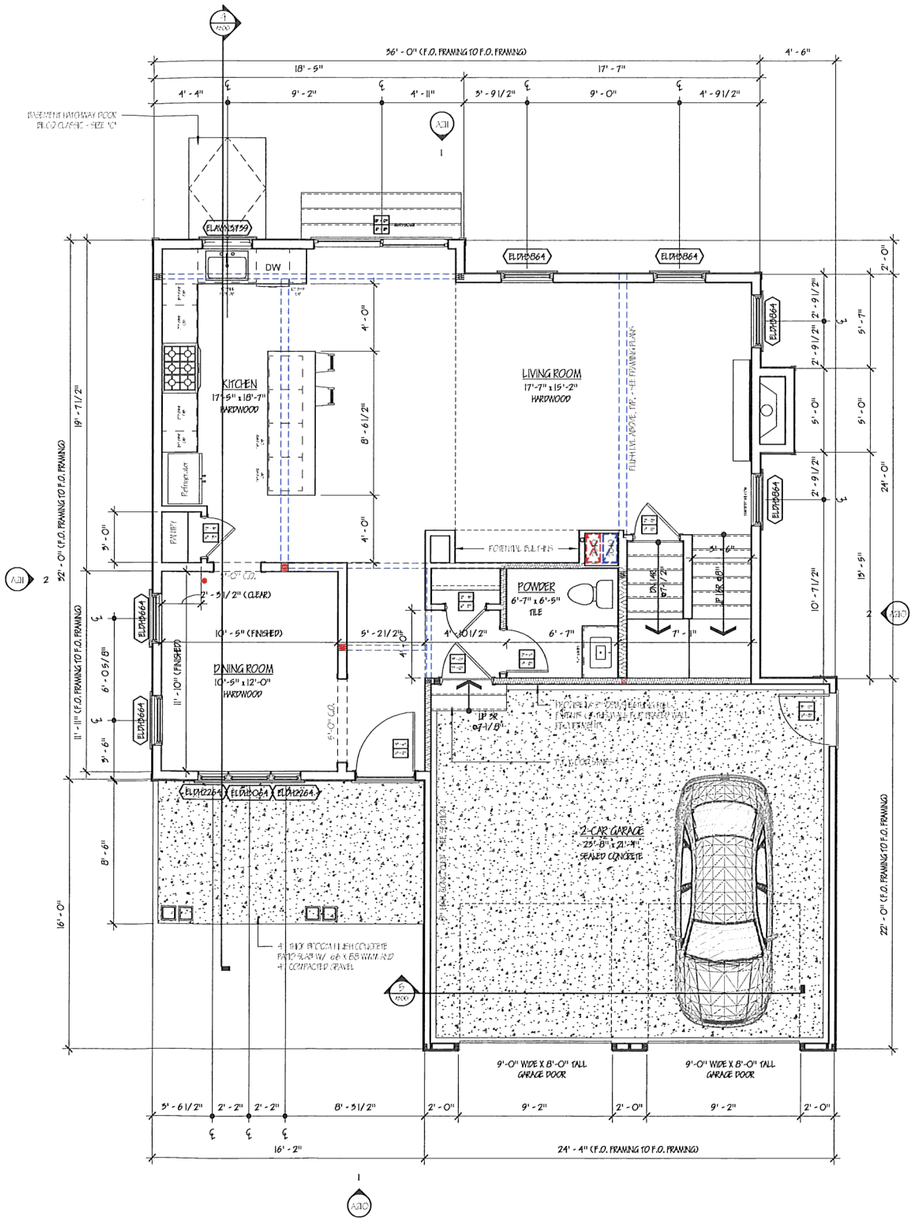

1 1ST FLOOR PLAN
SCALE: 1/4" = 1'-0"

dream developers

PROJECT NAME AND ADDRESS REDACTED

FOR PERMIT

SHEET TITLE:

CONSTRUCTION PLAN - 1ST AND 2ND FLOOR

HISTORY OF SUBMISSIONS:

4	PERMIT SET	2.14.2023
3	PLAN REVISIONS PER CLIENT REQUEST	2.7.2023
2	PLAN REVISIONS PER CLIENT COMMENTS	1.17.2023
1	INITIAL PLANS TO CLIENT	1.14.2023
#	ISSUE	DATE

PROJECT NO: 21.002	DATE: 2.14.2023
DRAWN: CDL	SCALE: As indicated

DRAWING NO:

A101